
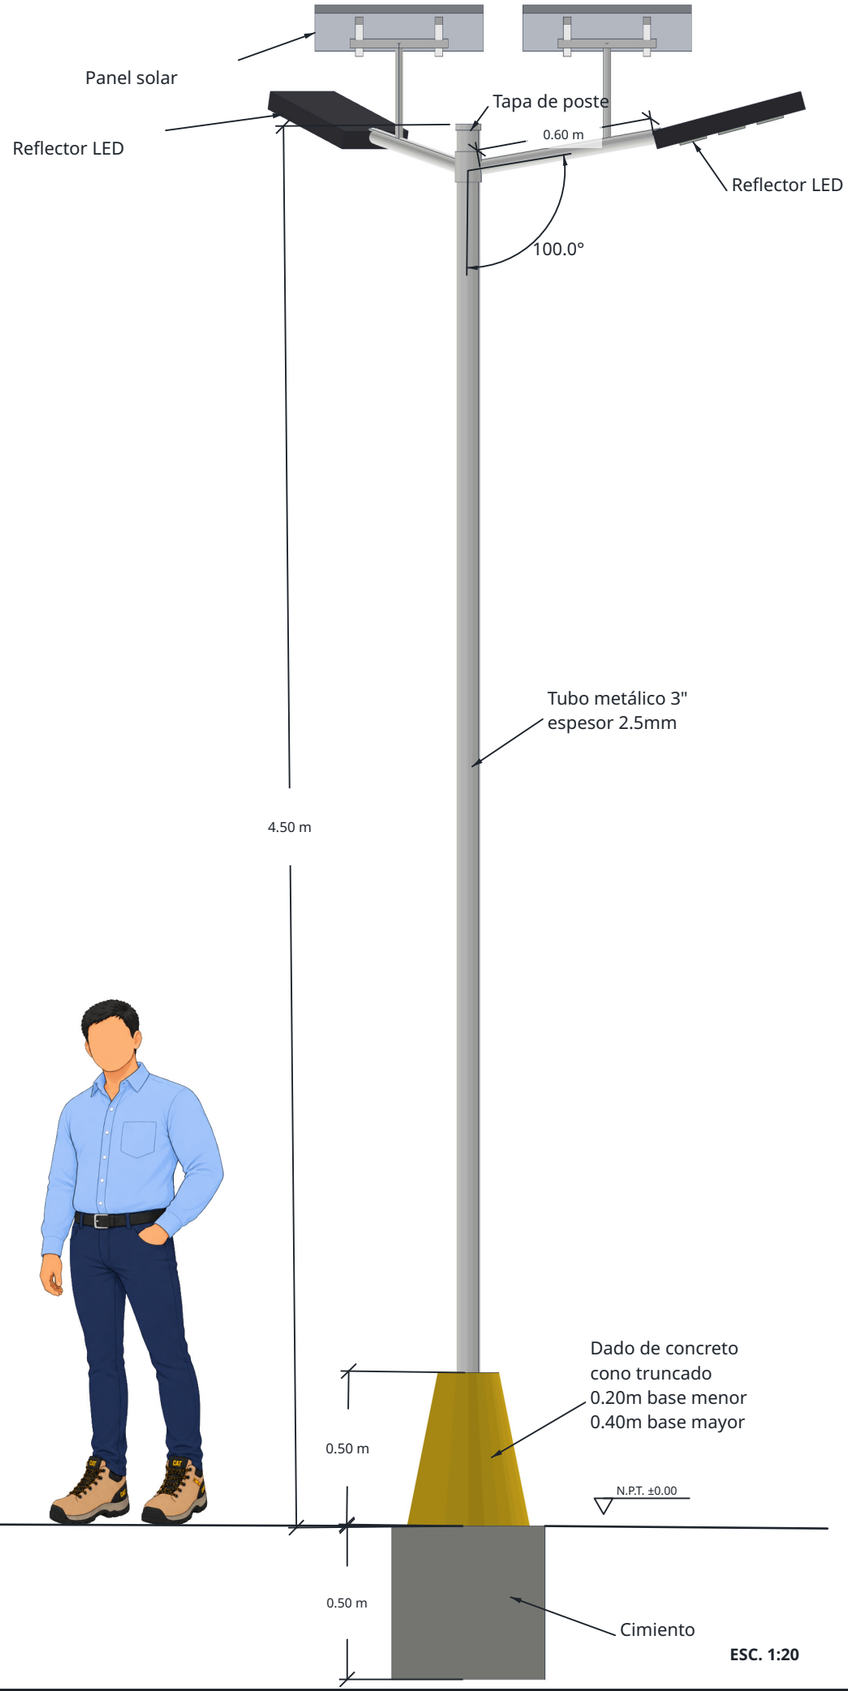




ESC. 1:20

VISTA DE PLANTA

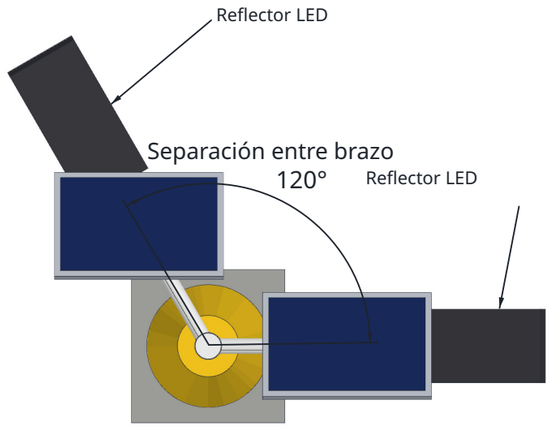



ESC. 1:20

DETALLE DADO Y CIMIENTO

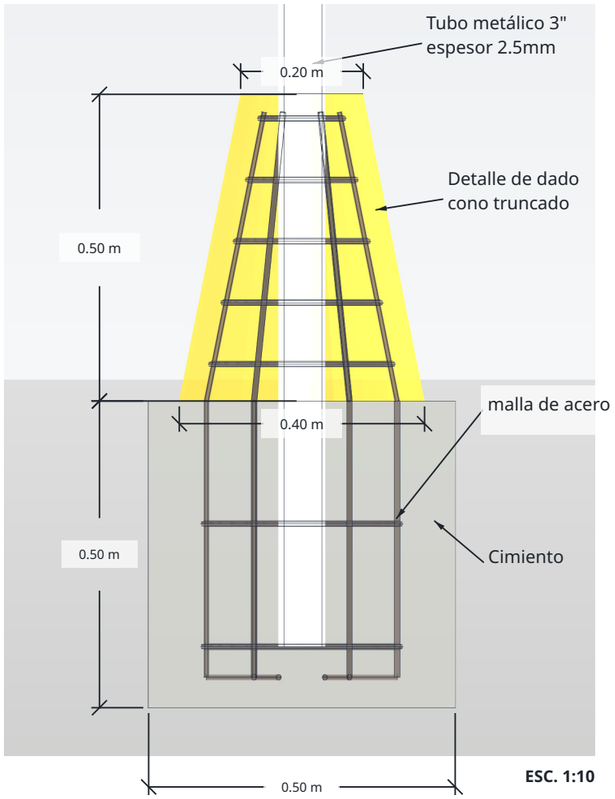


ESC. 1:10

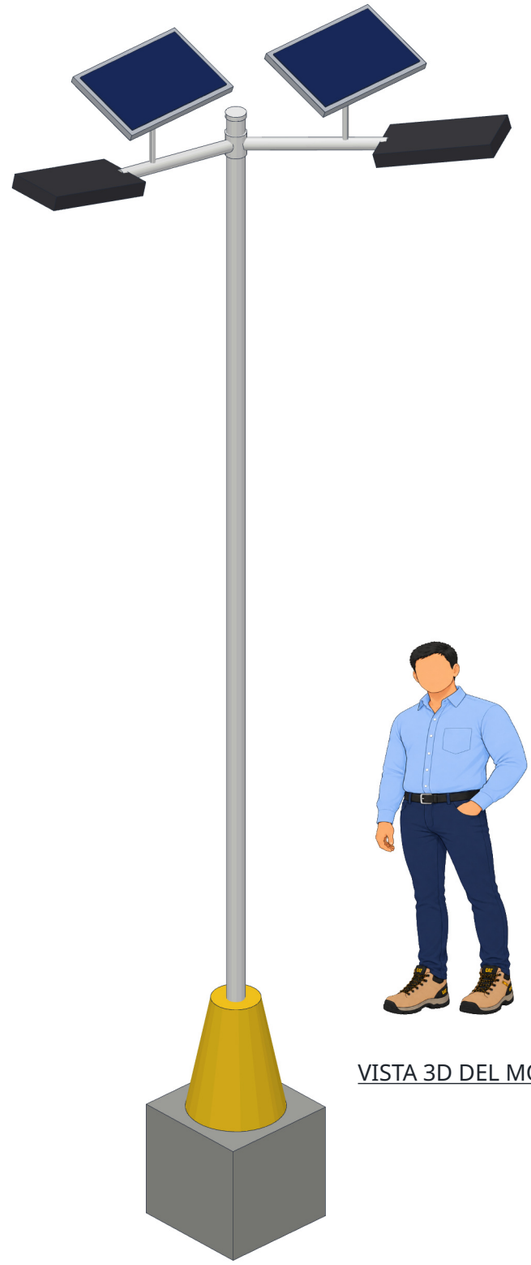

VISTA 3D DEL MODELO

| | |
|---|---|
| **PROYECTO** | CREACION DE LOS SERVICIOS DE ESPACIOS PÚBLICOS URBANOS EN LA PLAZA PRINCIPAL DE YANQUE DISTRITO DE CHICHAS DE LA PROVINCIA DE CONDESUYOS DEL DEPARTAMENTO DE AREQUIPA |
| **AUTOR** | MUNICIPALIDAD DISTRITAL DE CHICHAS |
| **FECHA** | JUNIO 2026 |
| **ESCALA** | INDICADA |
| **LÁMINA** | D03 - DETALLES DE LUMINARIAS SOLARES |